




| REV | DESCRIPTION               | DATE       |
|-----|---------------------------|------------|
| 0   | Hardware concept RL-MB-01 | 2026-10-05 |

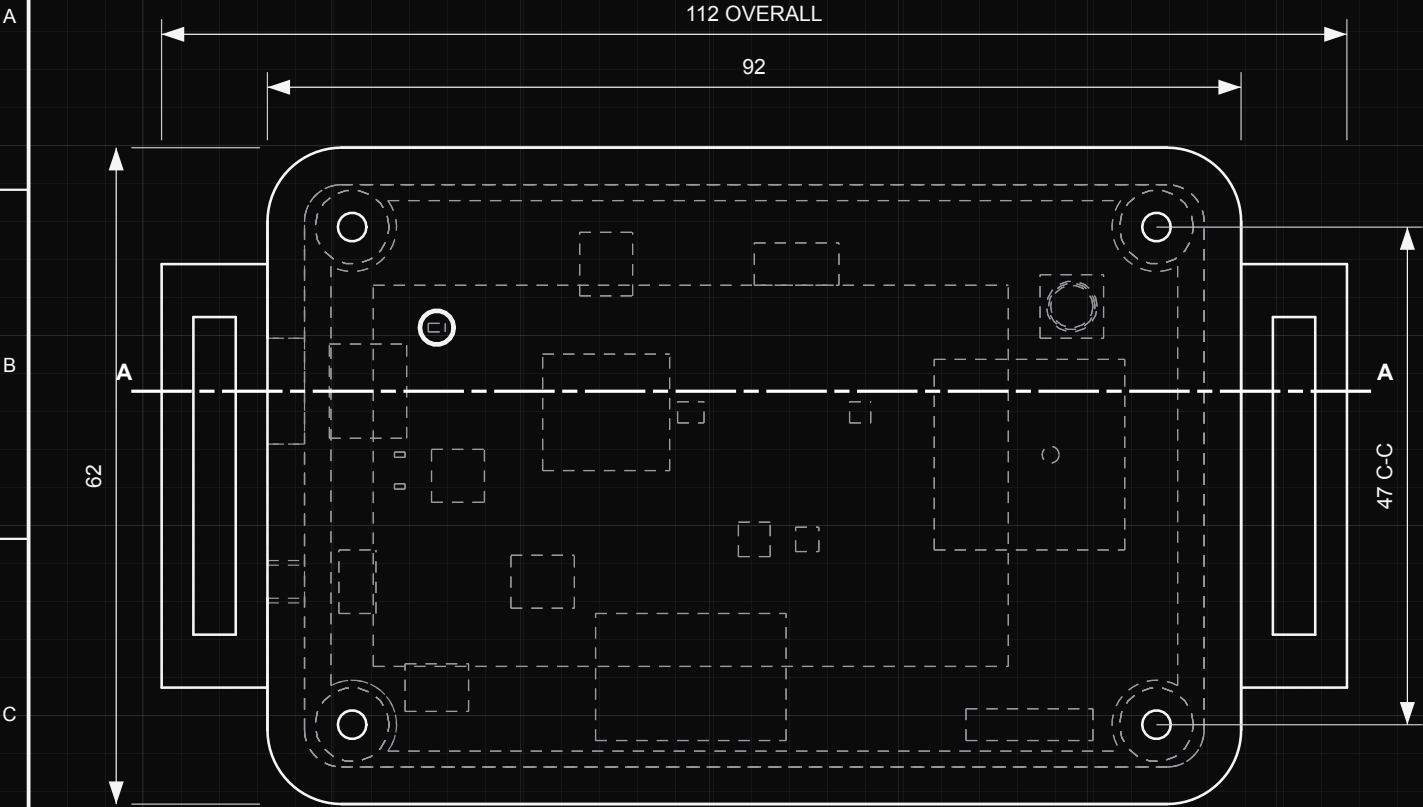


PLAN VIEW (LID SHOWN TRANSPARENT) / 1.4:1

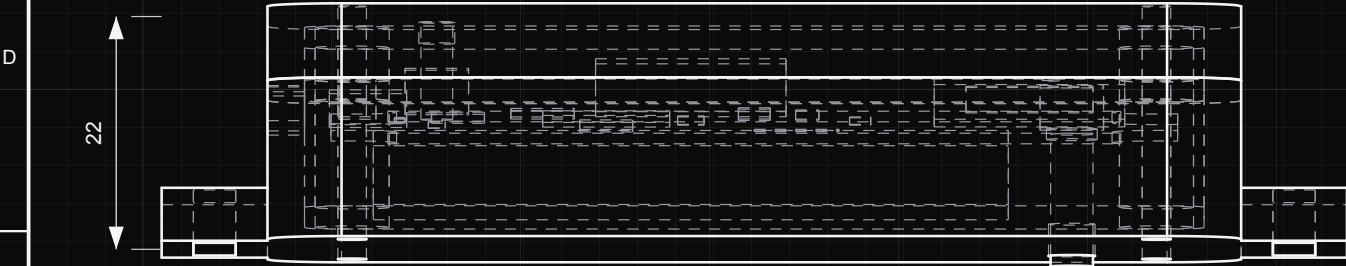

FRONT ELEVATION

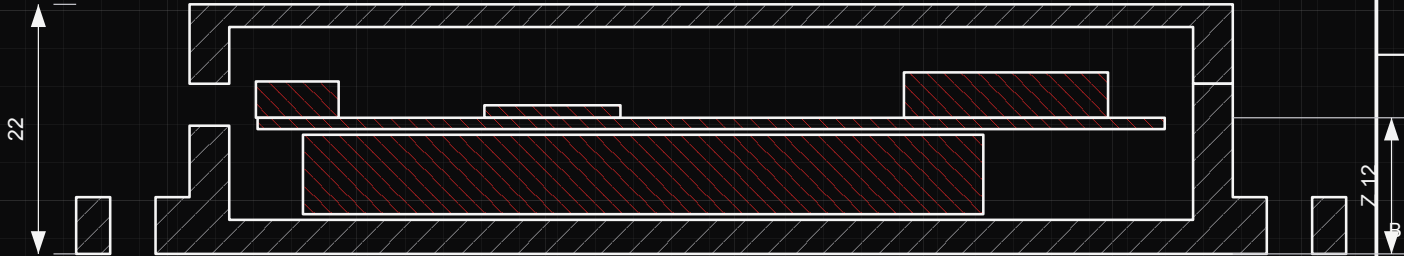

SECTION A-A / Y = +8 / 1.5:1  
Enclosure white hatch, electronics red hatch (PCB1, U1, U7, J1, BT1)

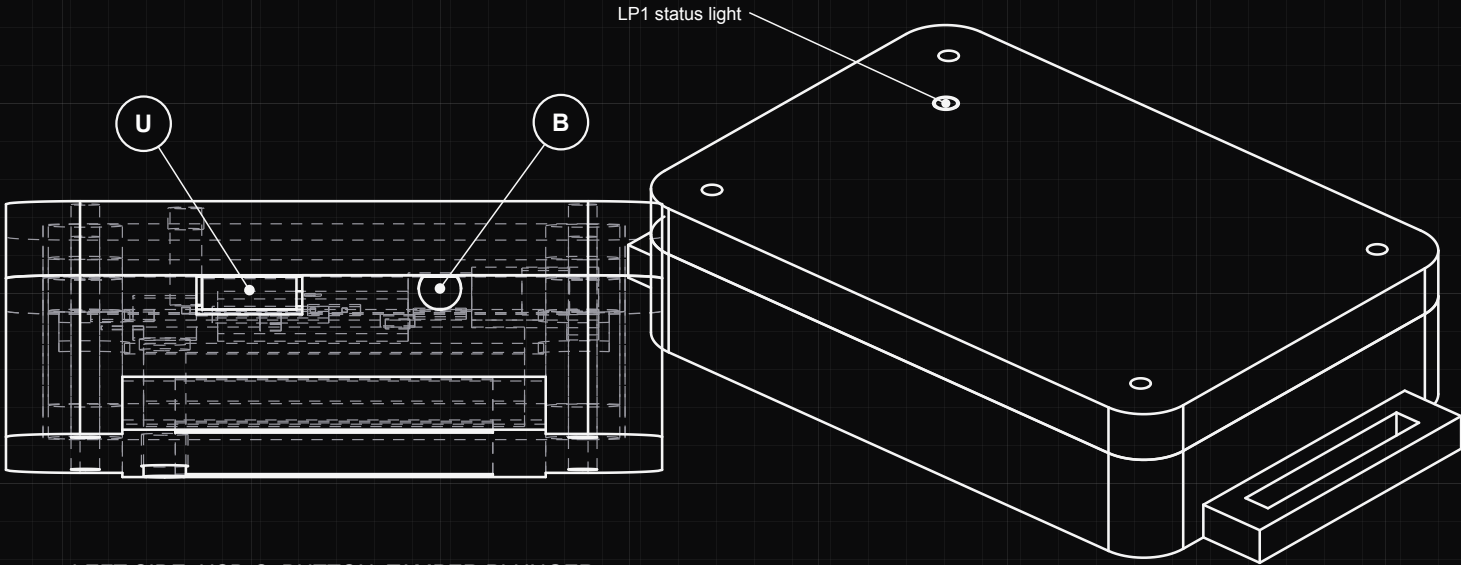

LEFT SIDE: USB-C, BUTTON, TAMPER PLUNGER

U USB-C opening 10 x 4.6 (charge only), silicone plug  
B hole D4 for SW1, membrane to be added

GENERAL NOTES

- Dimensions in mm. Third-angle projection. General tolerances to be defined (ISO 2768-m proposed).
- Board outlines: maker or distributor data cited in hardware/netlist.json; others are indicative envelopes.
- Heights, connectors and positions of openings are indicative and must be measured on the chosen parts.
- Geometry and sheets generated by cad/generate.py (build123d 0.13.0); checks run with --check.

GENERAL ASSEMBLY

Redline tracker and black box, board RL-MB-01 (nRF9151)

| DRAWING NO.          | SCALE              | REV                     | SHEET |
|----------------------|--------------------|-------------------------|-------|
| RL-HW-01             | 1.4:1 unless noted | 0                       | 1 / 5 |
| DRAWN BY: M. ABAAQIL | DATE: 2026-10-05   | MATERIAL: to be defined |       |